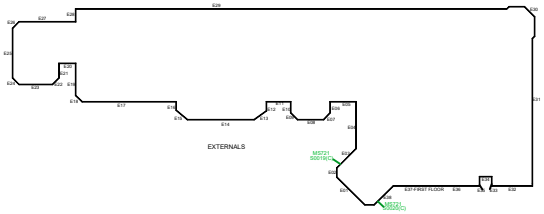

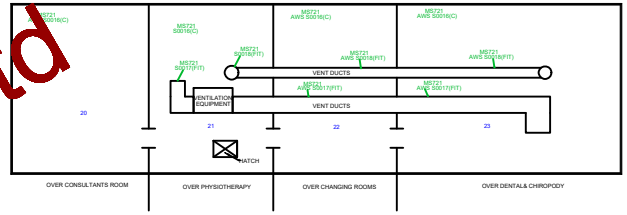

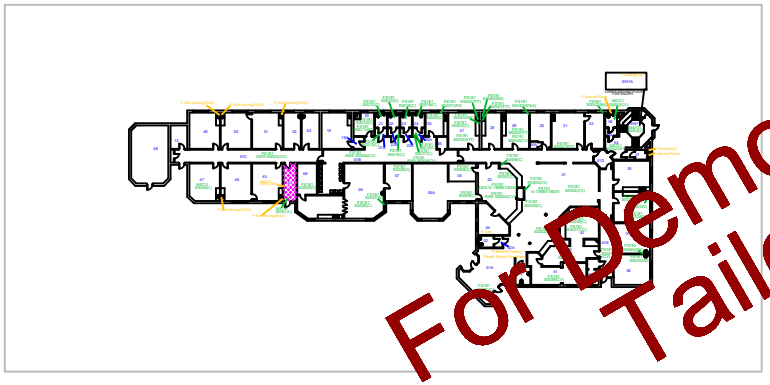

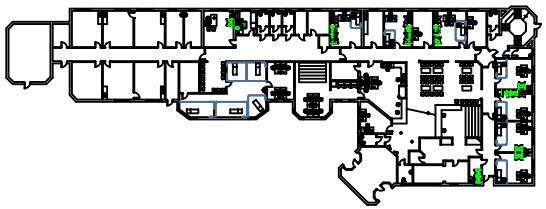

For Demonstration Purposes Only
Tailor Made Software, Ltd

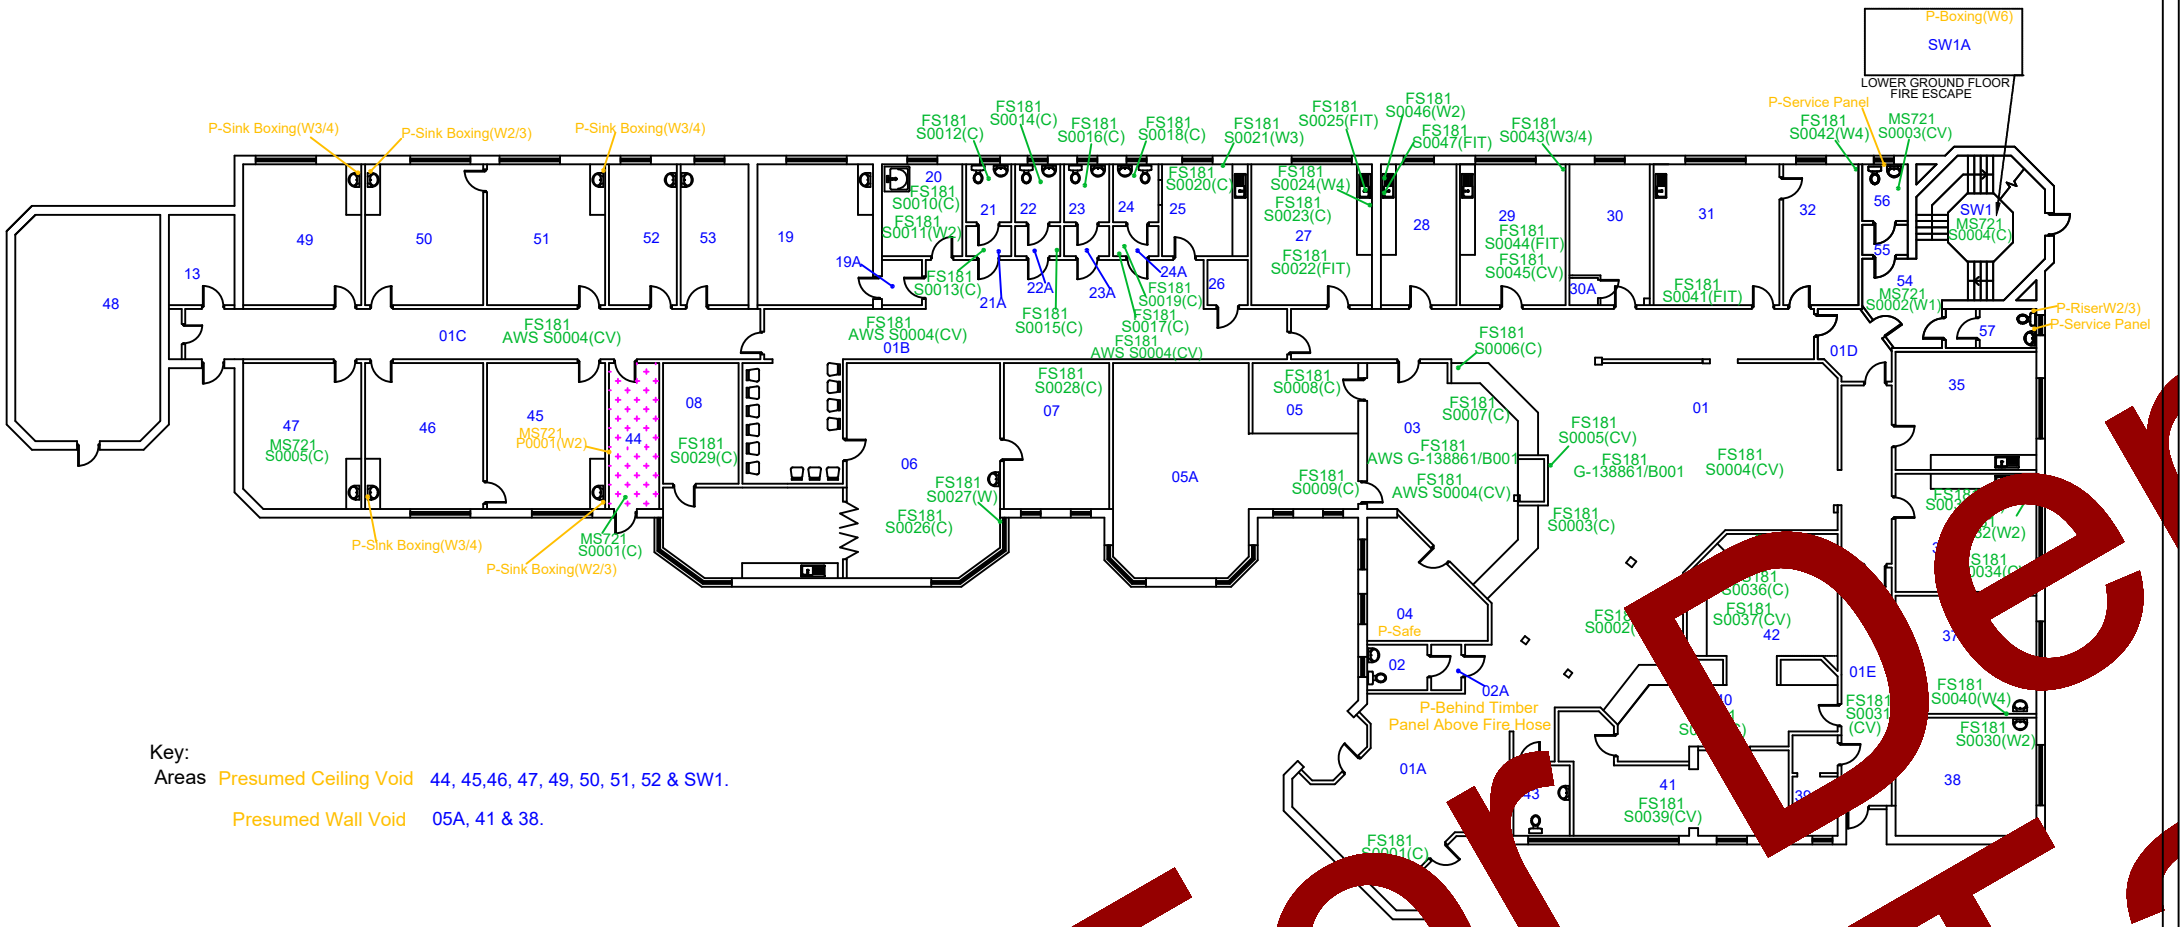

Key:

Areas Presumed Ceiling Void 44, 45,46, 47, 49, 50, 51, 52 & SW1.

Presumed Wall Void 05A, 41 & 38.

For Dem
Tr

SAMPLE DRAWING

12 Some Street
Industrial Estate
West Town
127 40
Tel: 0123-56789
Fax: 0123-98765
Web: www.myweb.com

Client: My Client Name	Ref: PR1111/ MS777 FS888 FS999
Job No: Y17-111111111	Date: 30/06/16
Site Address: The Client Site Building	Scale: NTS
	Drawn by: J.D.
	Page 1 of 1

Key 1: 01 Room ID

EXT External Number

Key 2: Sample Results

S0001 Negative

S0001 Positive

AWS Associated with Sample

P/SP Presumed/Strongly Presumed

Key 3: No Access/Presumed

Not In Survey Remit

Room Contains ACM/ Strongly Presumed ACM